

SX-SO-SX

SLIDE BY SIDE

THREE PANEL | FULL BREAKOUT CENTER SIDELIGHT

Scale: 1/4" = 1'- 0" (elevations shown)

PROJECT INFORMATION

PROJECT NAME:


LOCATION:

JOB NUMBER:


DATE:

SHEET:


EXTERIOR ELEVATION — SX-SO-SX SLIDE BY SIDE

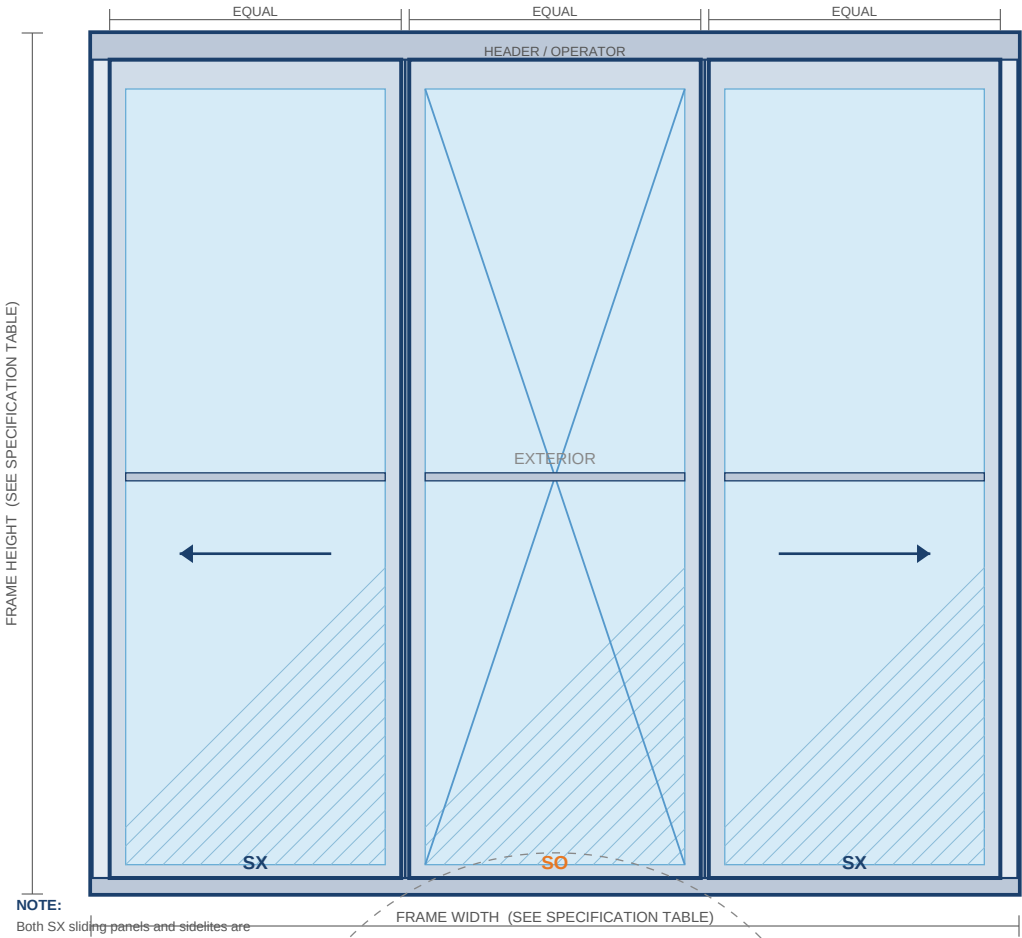

FLOOR PLAN

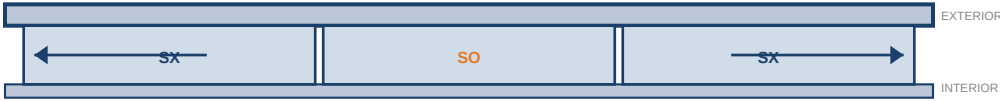

VERTICAL SECTION

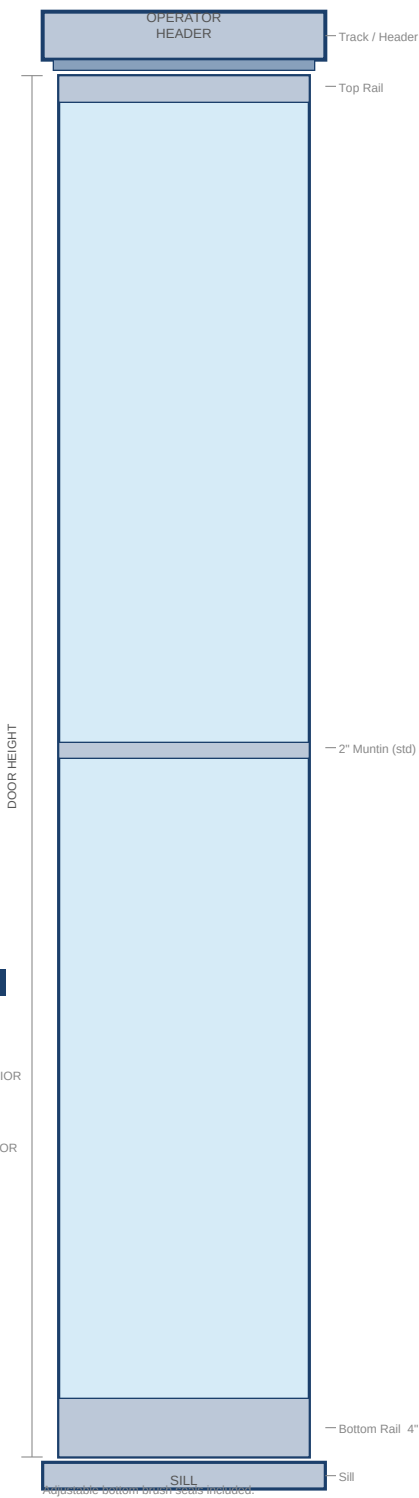

MODEL	CONFIGURATION	FRAME WIDTH	FRAME HEIGHT	CLEAR OPENING	ROUGH OPENING W	ROUGH OPENING H
DT-2100	SX-SO-SX	10'-8" (128")	7'6" — 8'0"	38" Net Slide	129"	Per height
DT-2100	SX-SO-SX	12'-0" (144")	7'6" — 8'0"	44" Net Slide	145"	Per height

Clear opening shown is for equal-panel standard configuration. Unequal panel splits available — call factory.