



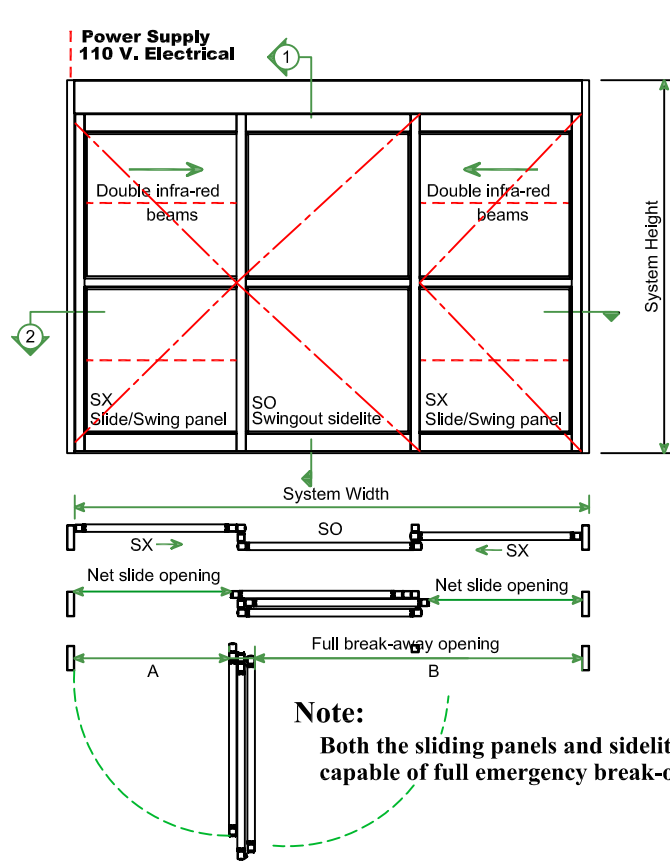


Elevation & floor plans
Exterior view elevation

Scale : 1/4" = 1'-0" | 10'-6" (3200) System shown

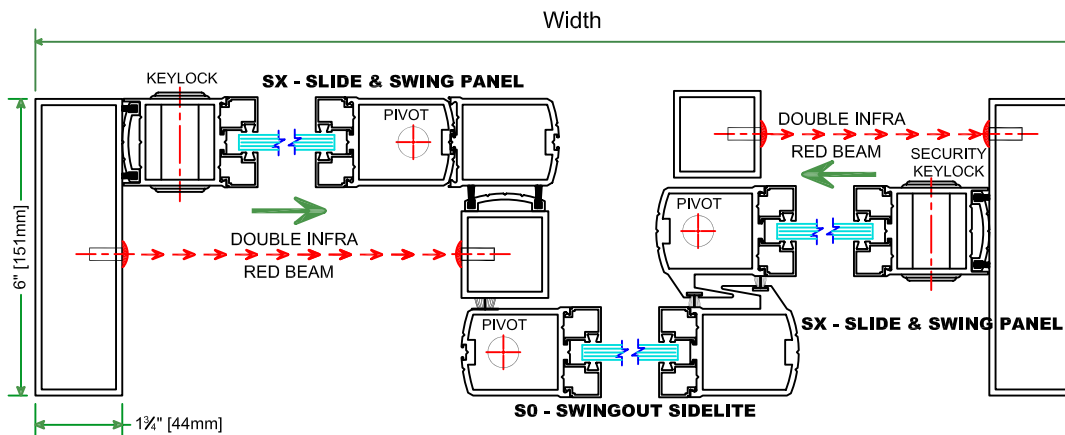


Glass options

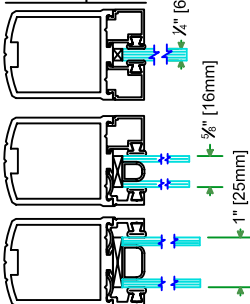

Model	System Width	System Height	Net Slide Opening	Vertical Opening	A Full Breakout Opening	B Full Breakout Opening	Wall Opening Width	Wall Opening Height
ES-22126	10'-6" (3200)	90" (2286)	36" (915)	82" (2083)	37'-1/2" (953)	77" (1956)	126'-1/2" (3212)	90'-1/4" (2292)
ES-22144	12'-0" (2743)	90" (2286)	42" (1067)	82" (2083)	43'-1/2" (1105)	89" (2261)	144'-1/2" (3670)	90'-1/4" (2292)

* Dimensions in imperial - Metric in parentheses.

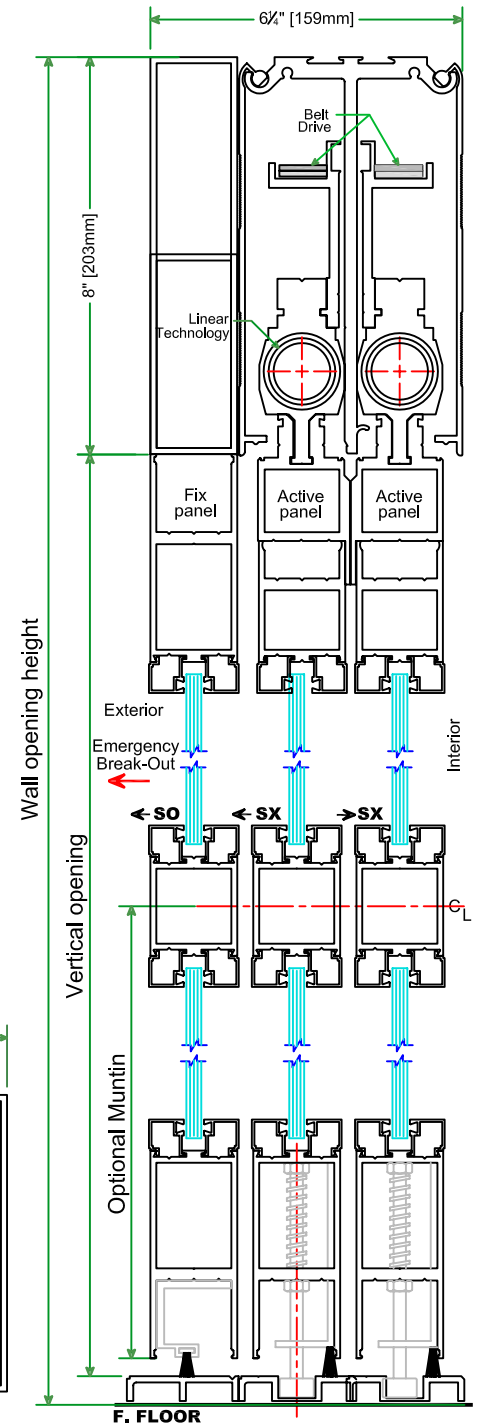

Adjustable bottom brushes
optional sill conditions available

2 Vertical Section

Door shown in open position
Scale : 3" = 1'-0"